


豊橋柳生川南部土地区画整理事業

重ね図（公図+現況+仮換地）

縮尺 500分の 1

1 街図

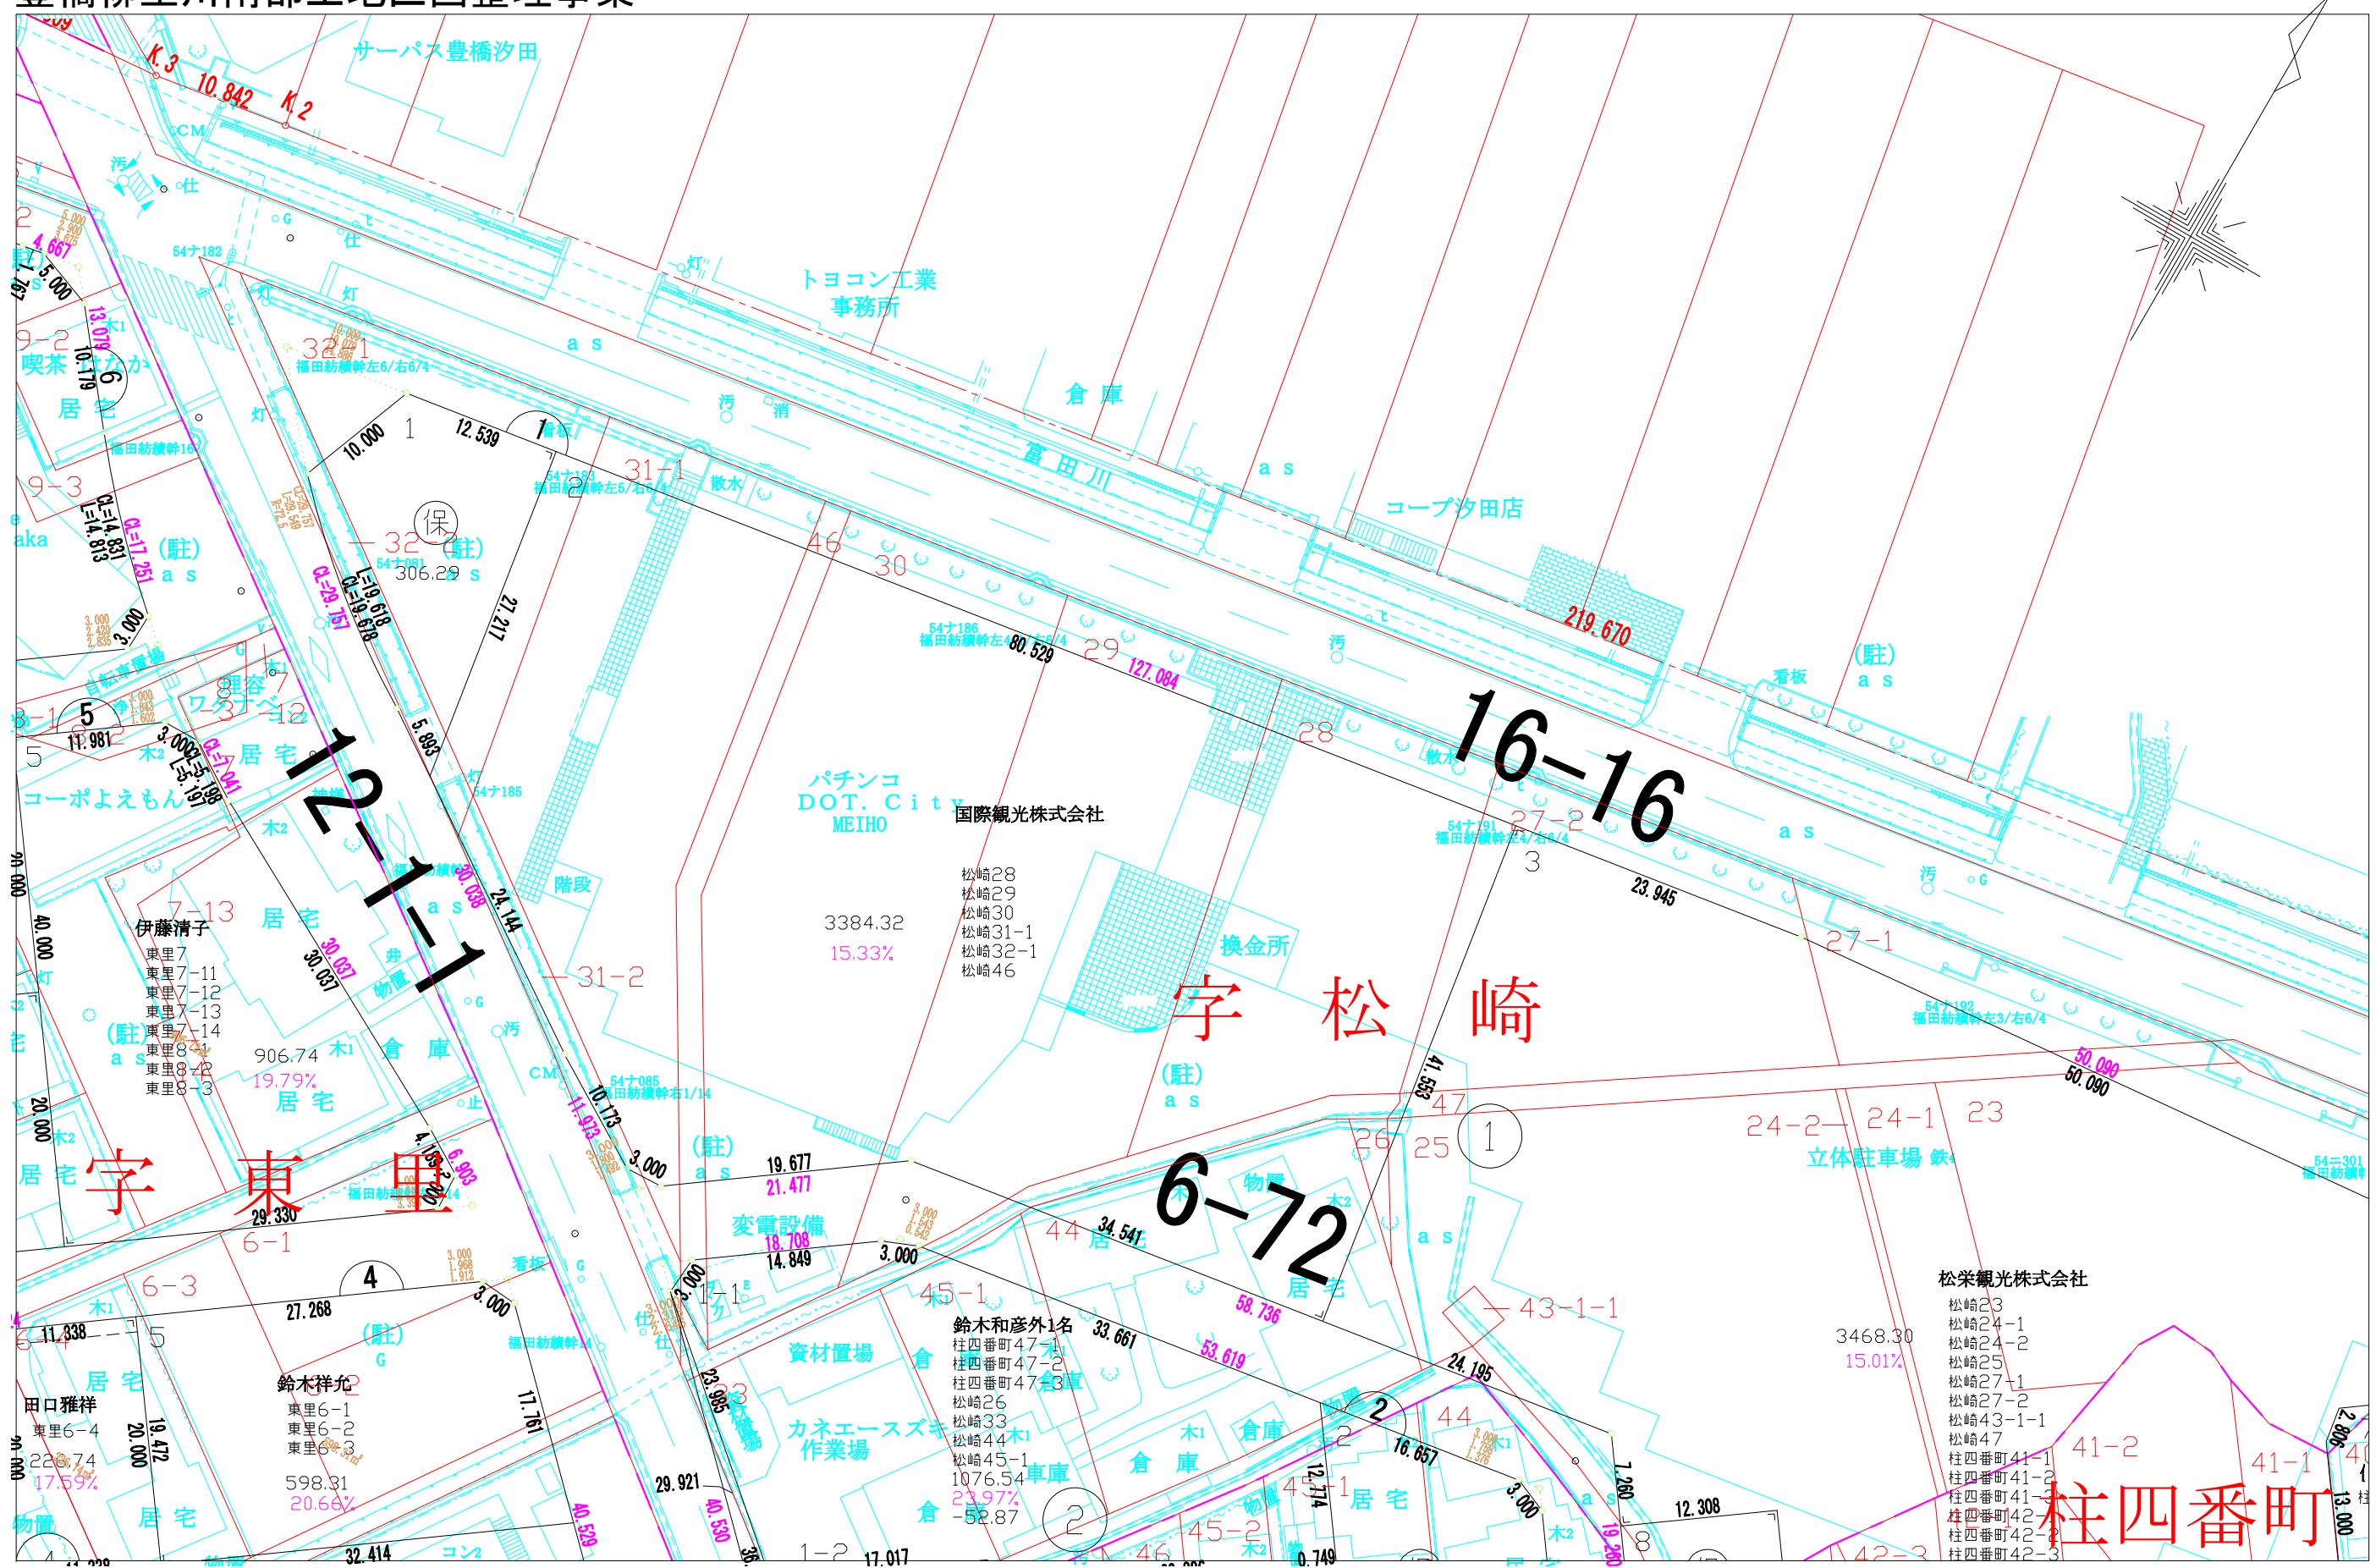


縮尺 500分の1

豊橋柳生川南部土地区画整理事業

重ね図(公図+現況+仮換地)

1街区

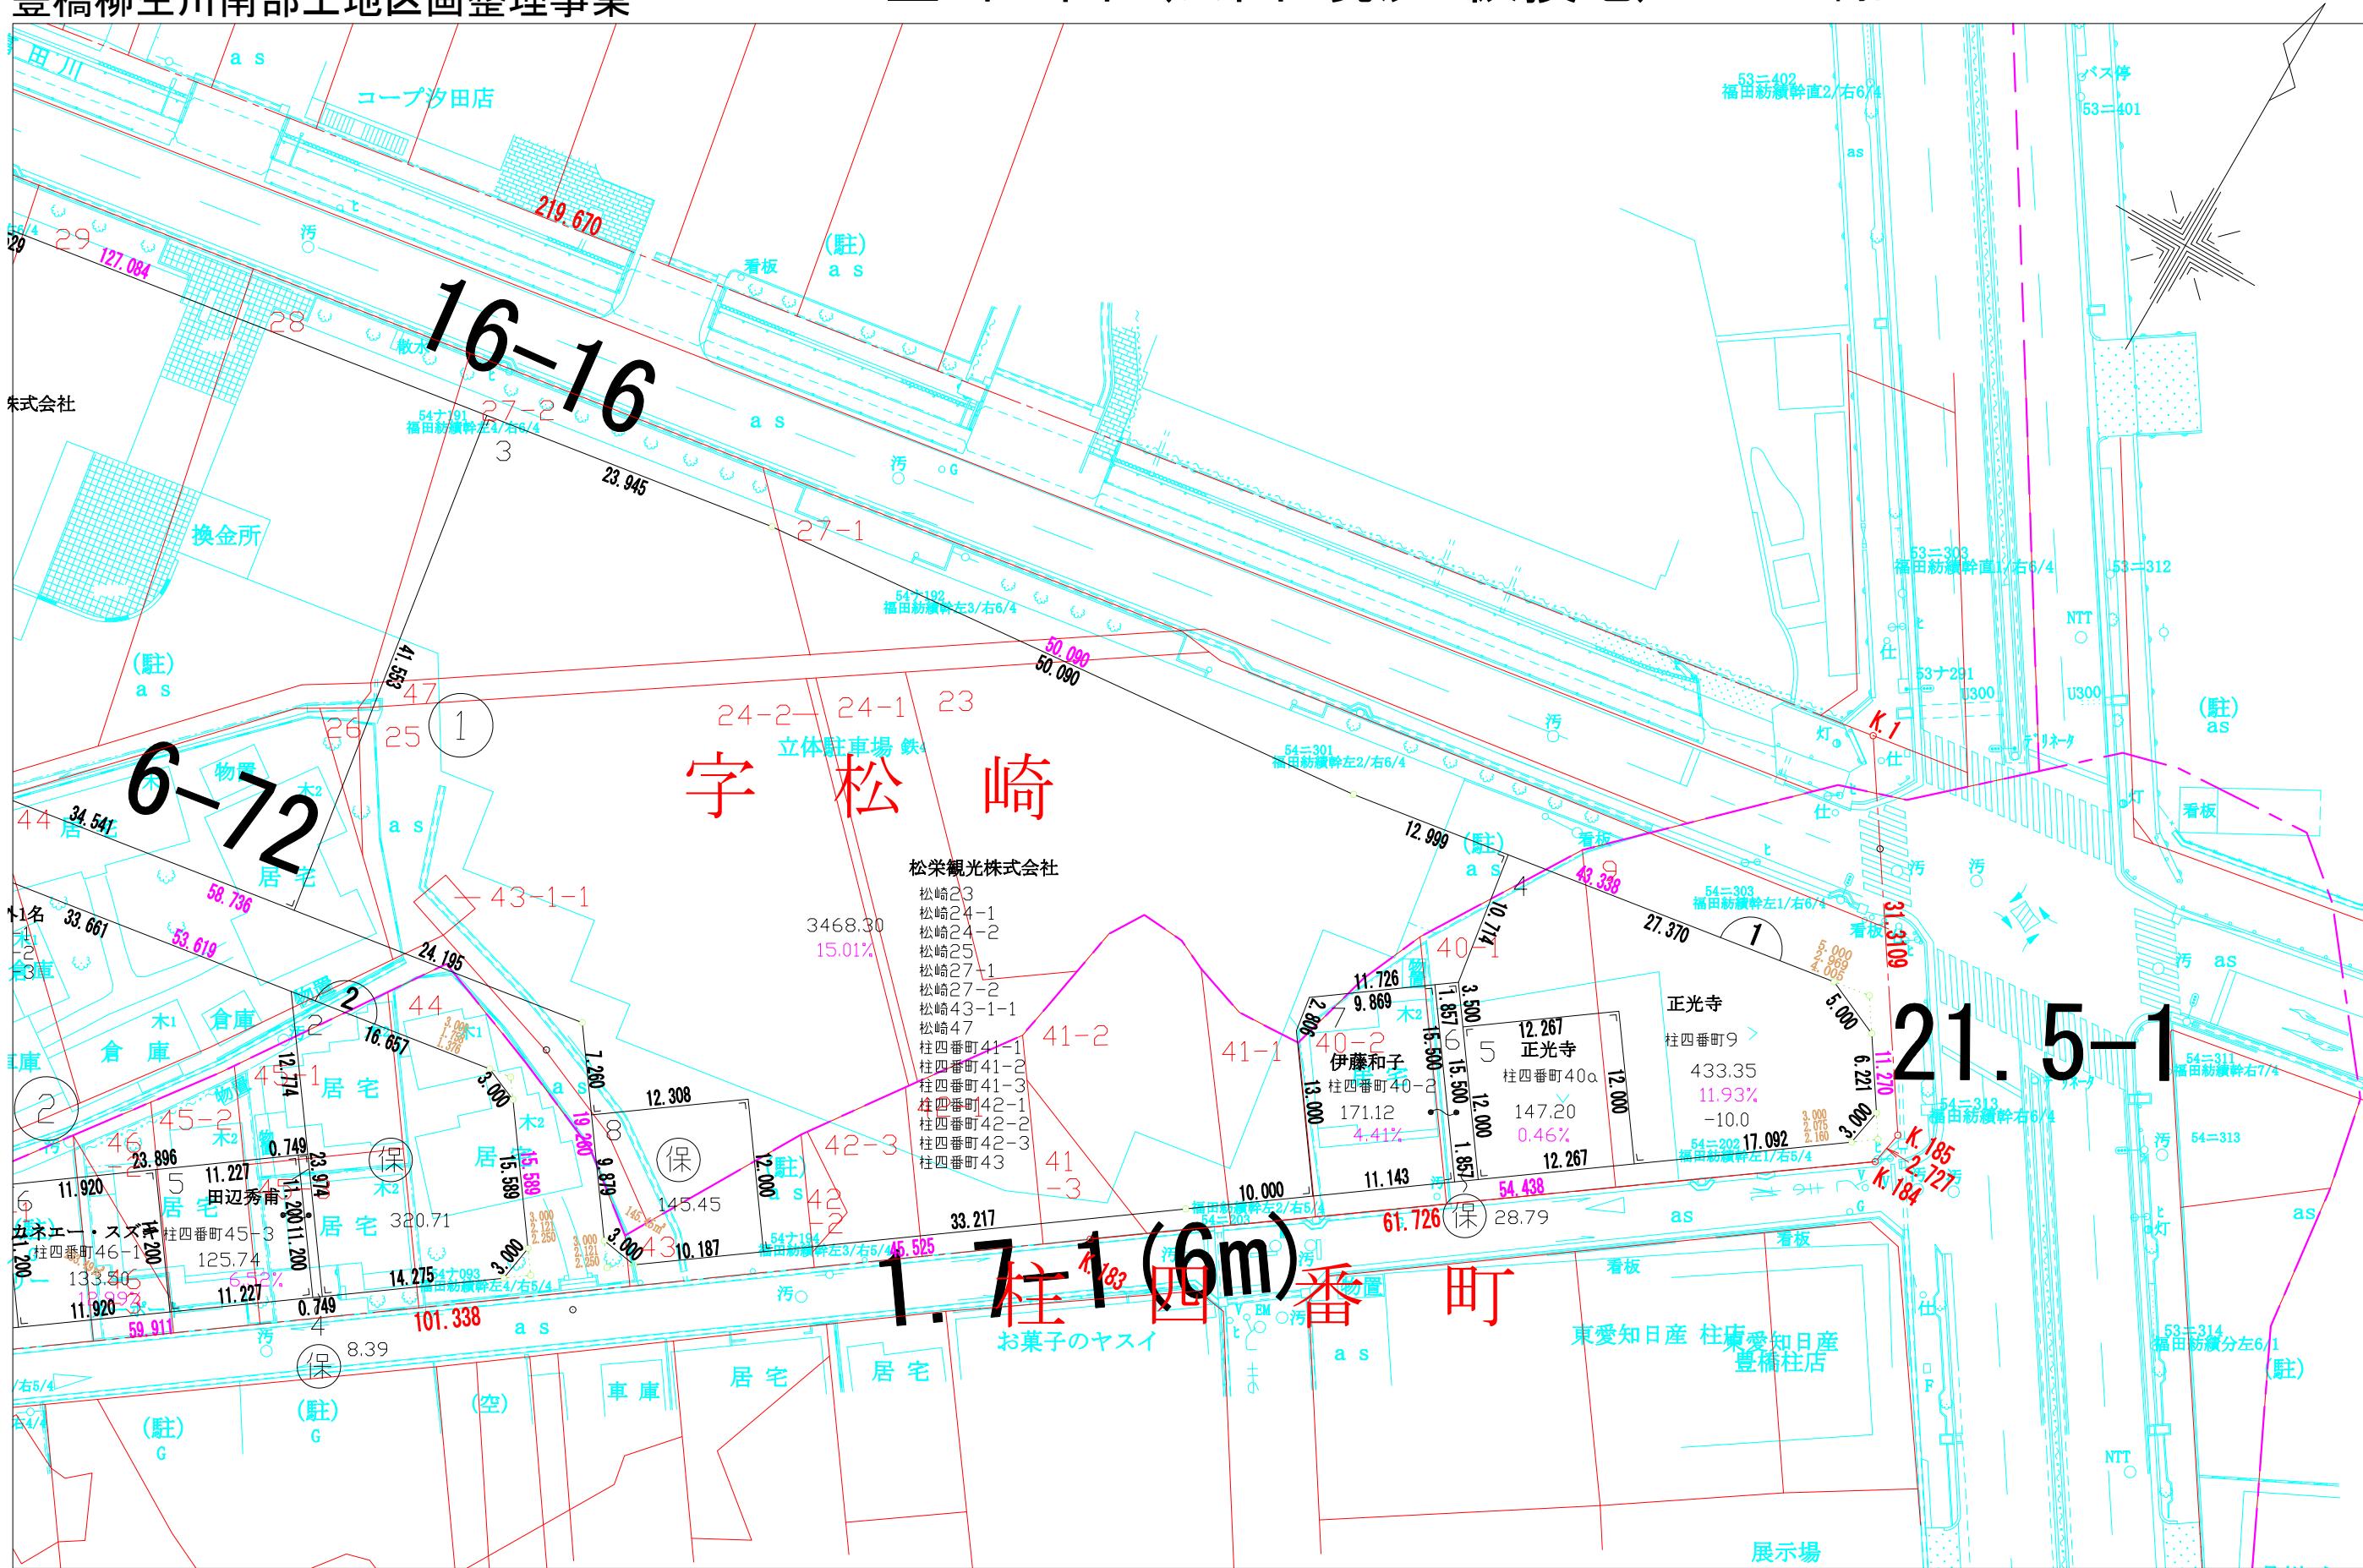


豊橋柳生川南部土地区画整理事業

重ね図（公図+現況+仮換地）

縮尺 500分の 1

2 街区

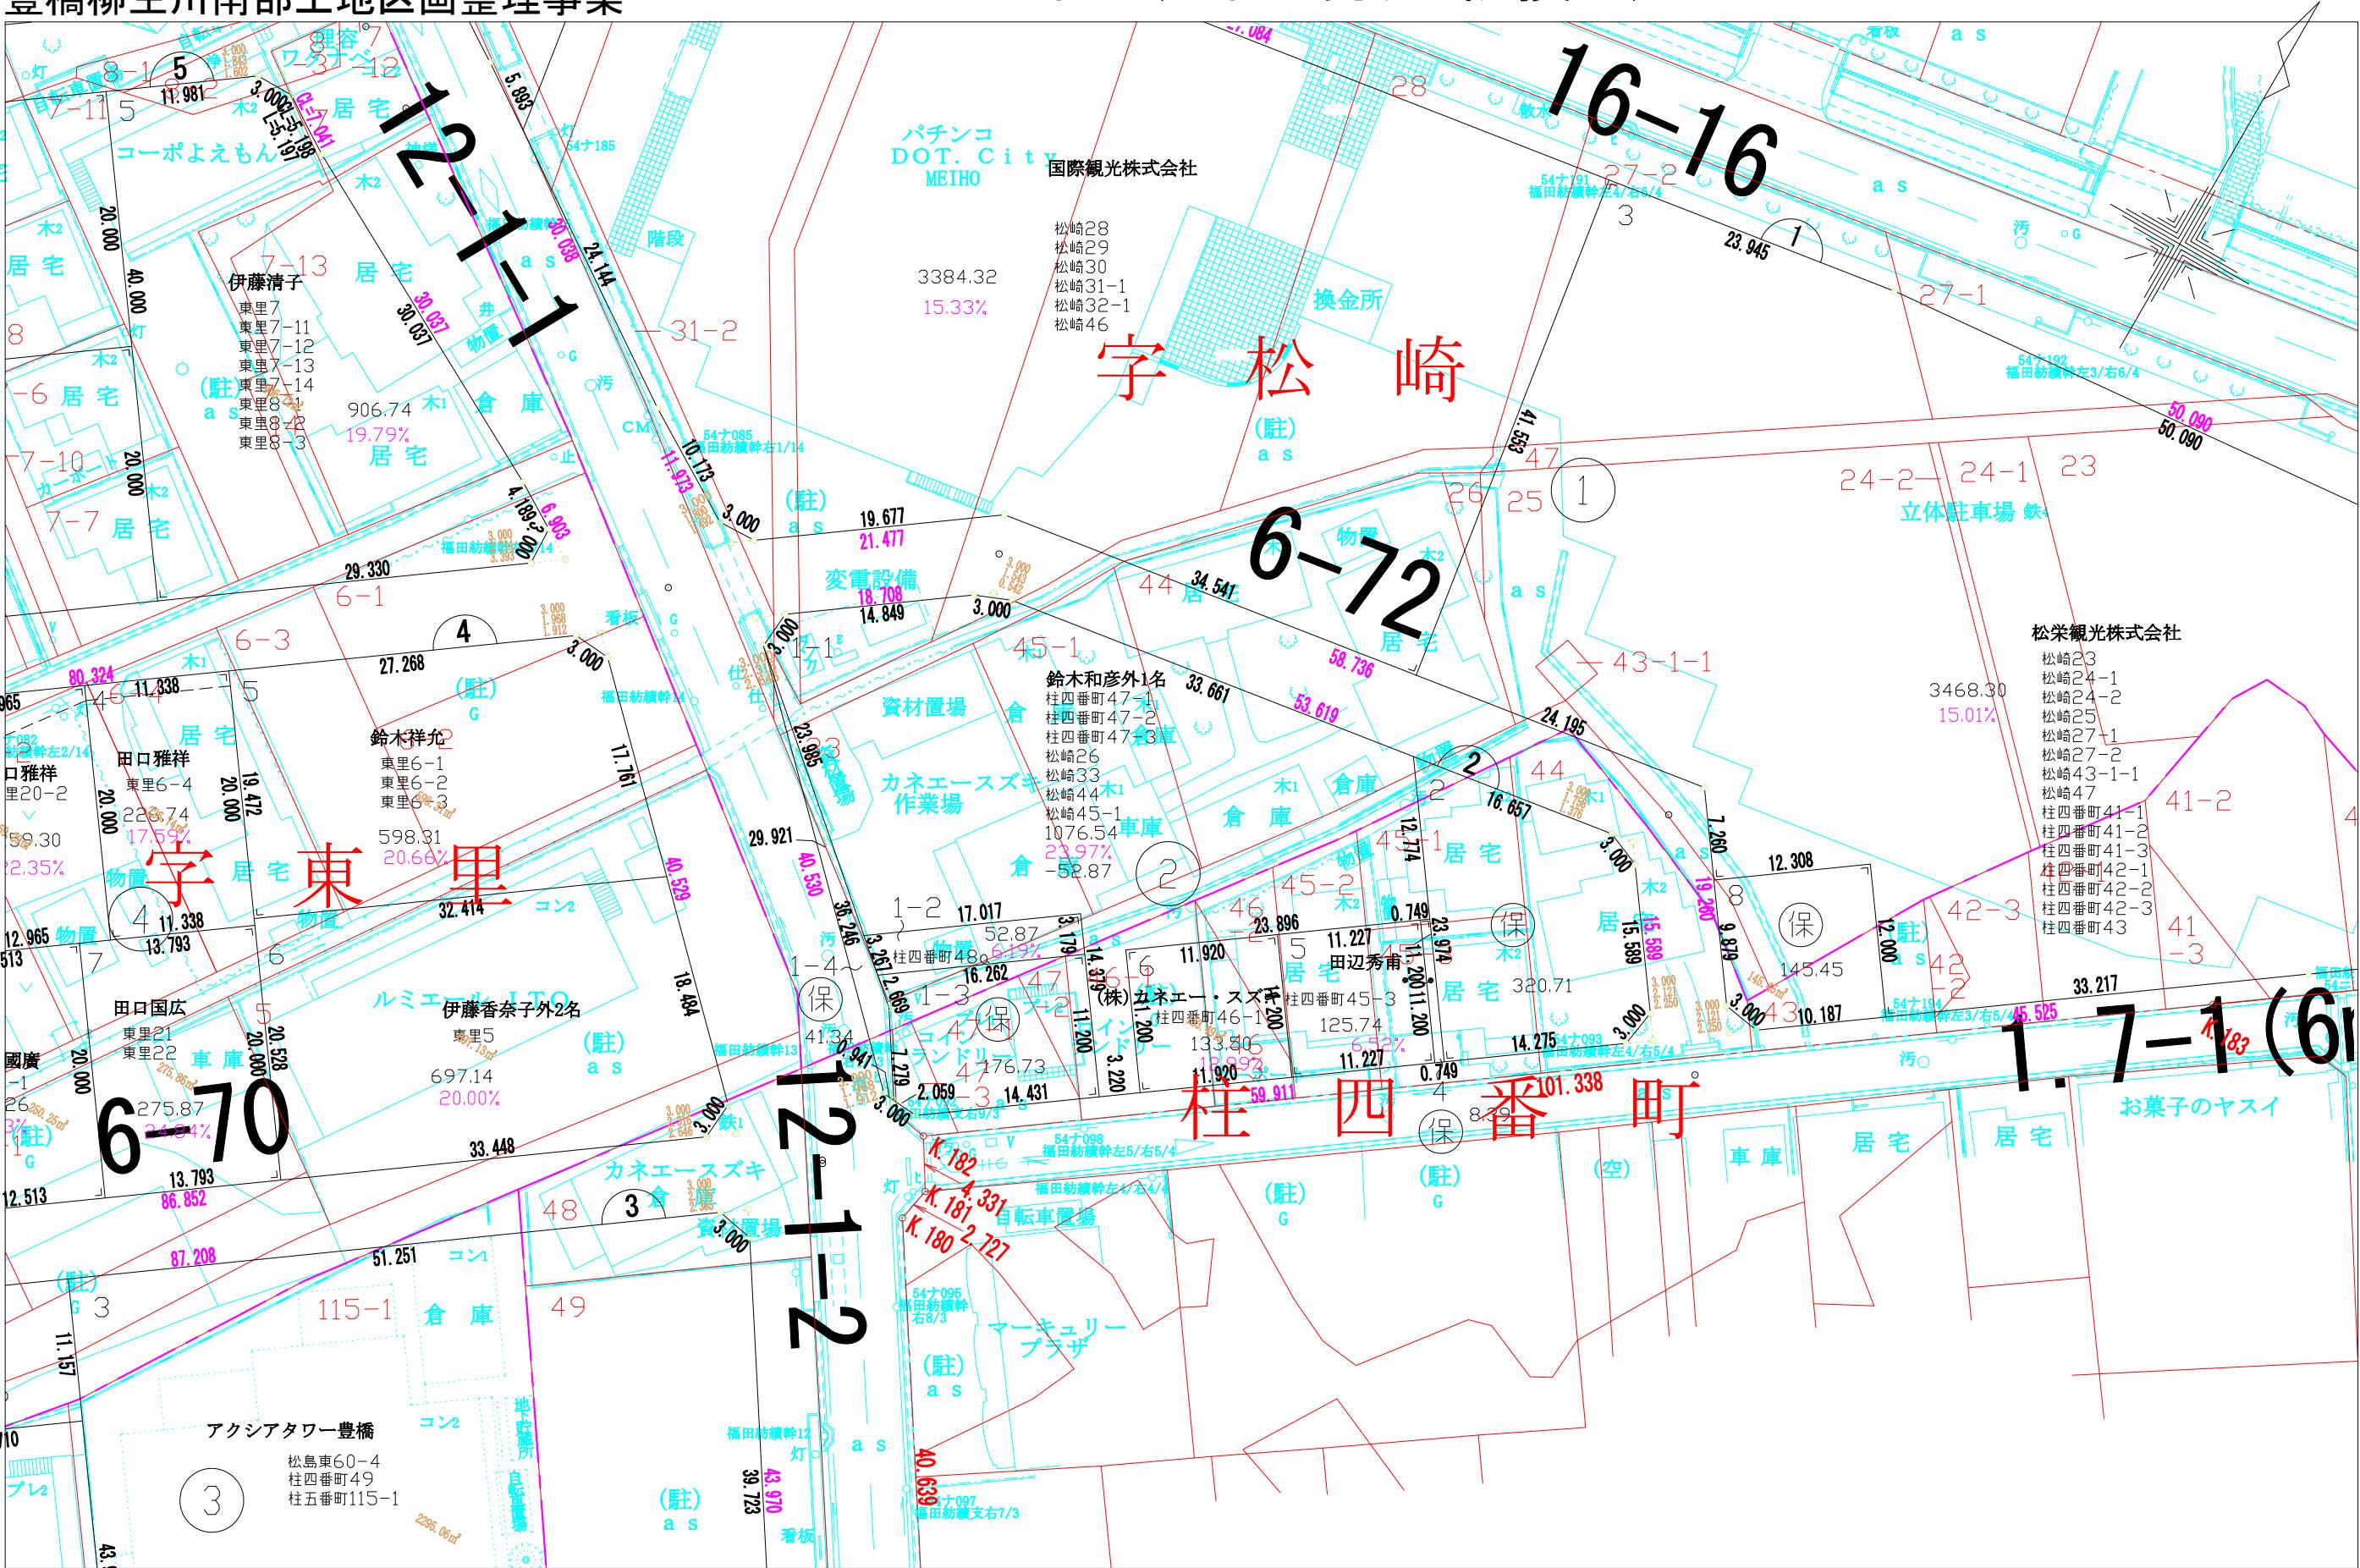


縮尺 500分の1

3 街区

重ね図(公図+現況+仮換地)

豊橋柳生川南部土地区画整理事業

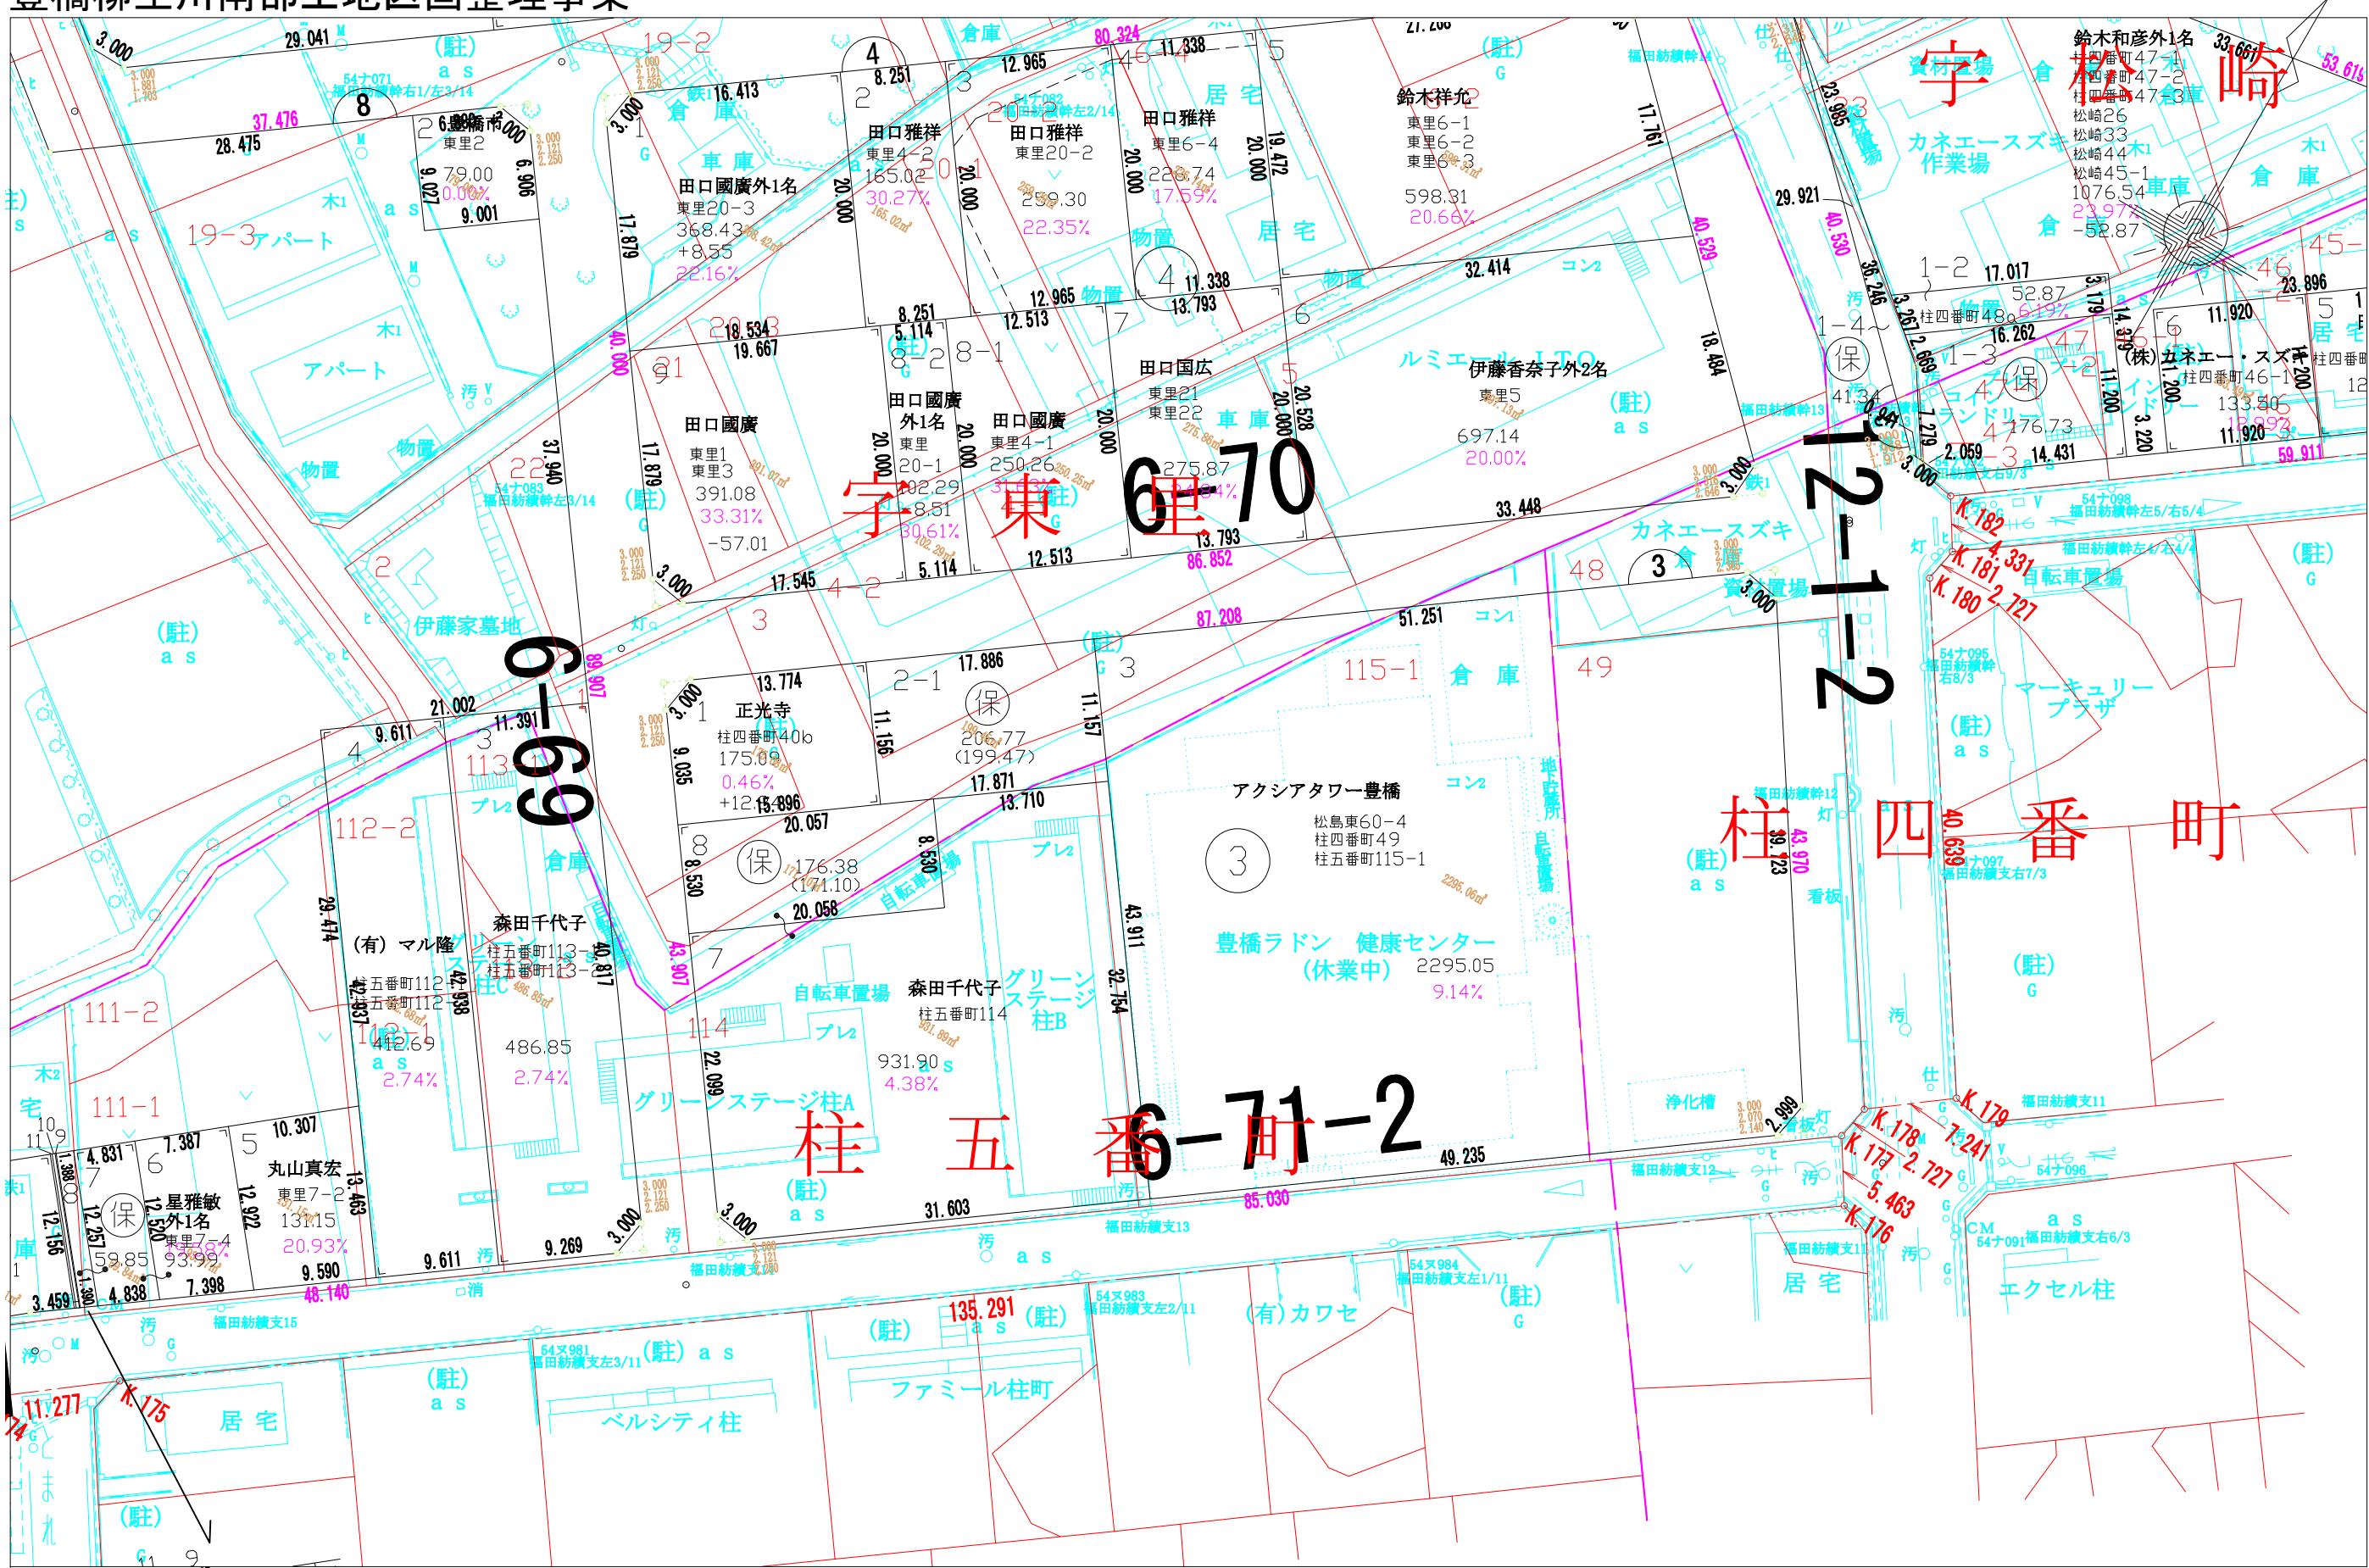


豊橋柳生川南部土地区画整理事業

重ね図（公図+現況+仮換地）

縮尺 500分の 1

4 街区

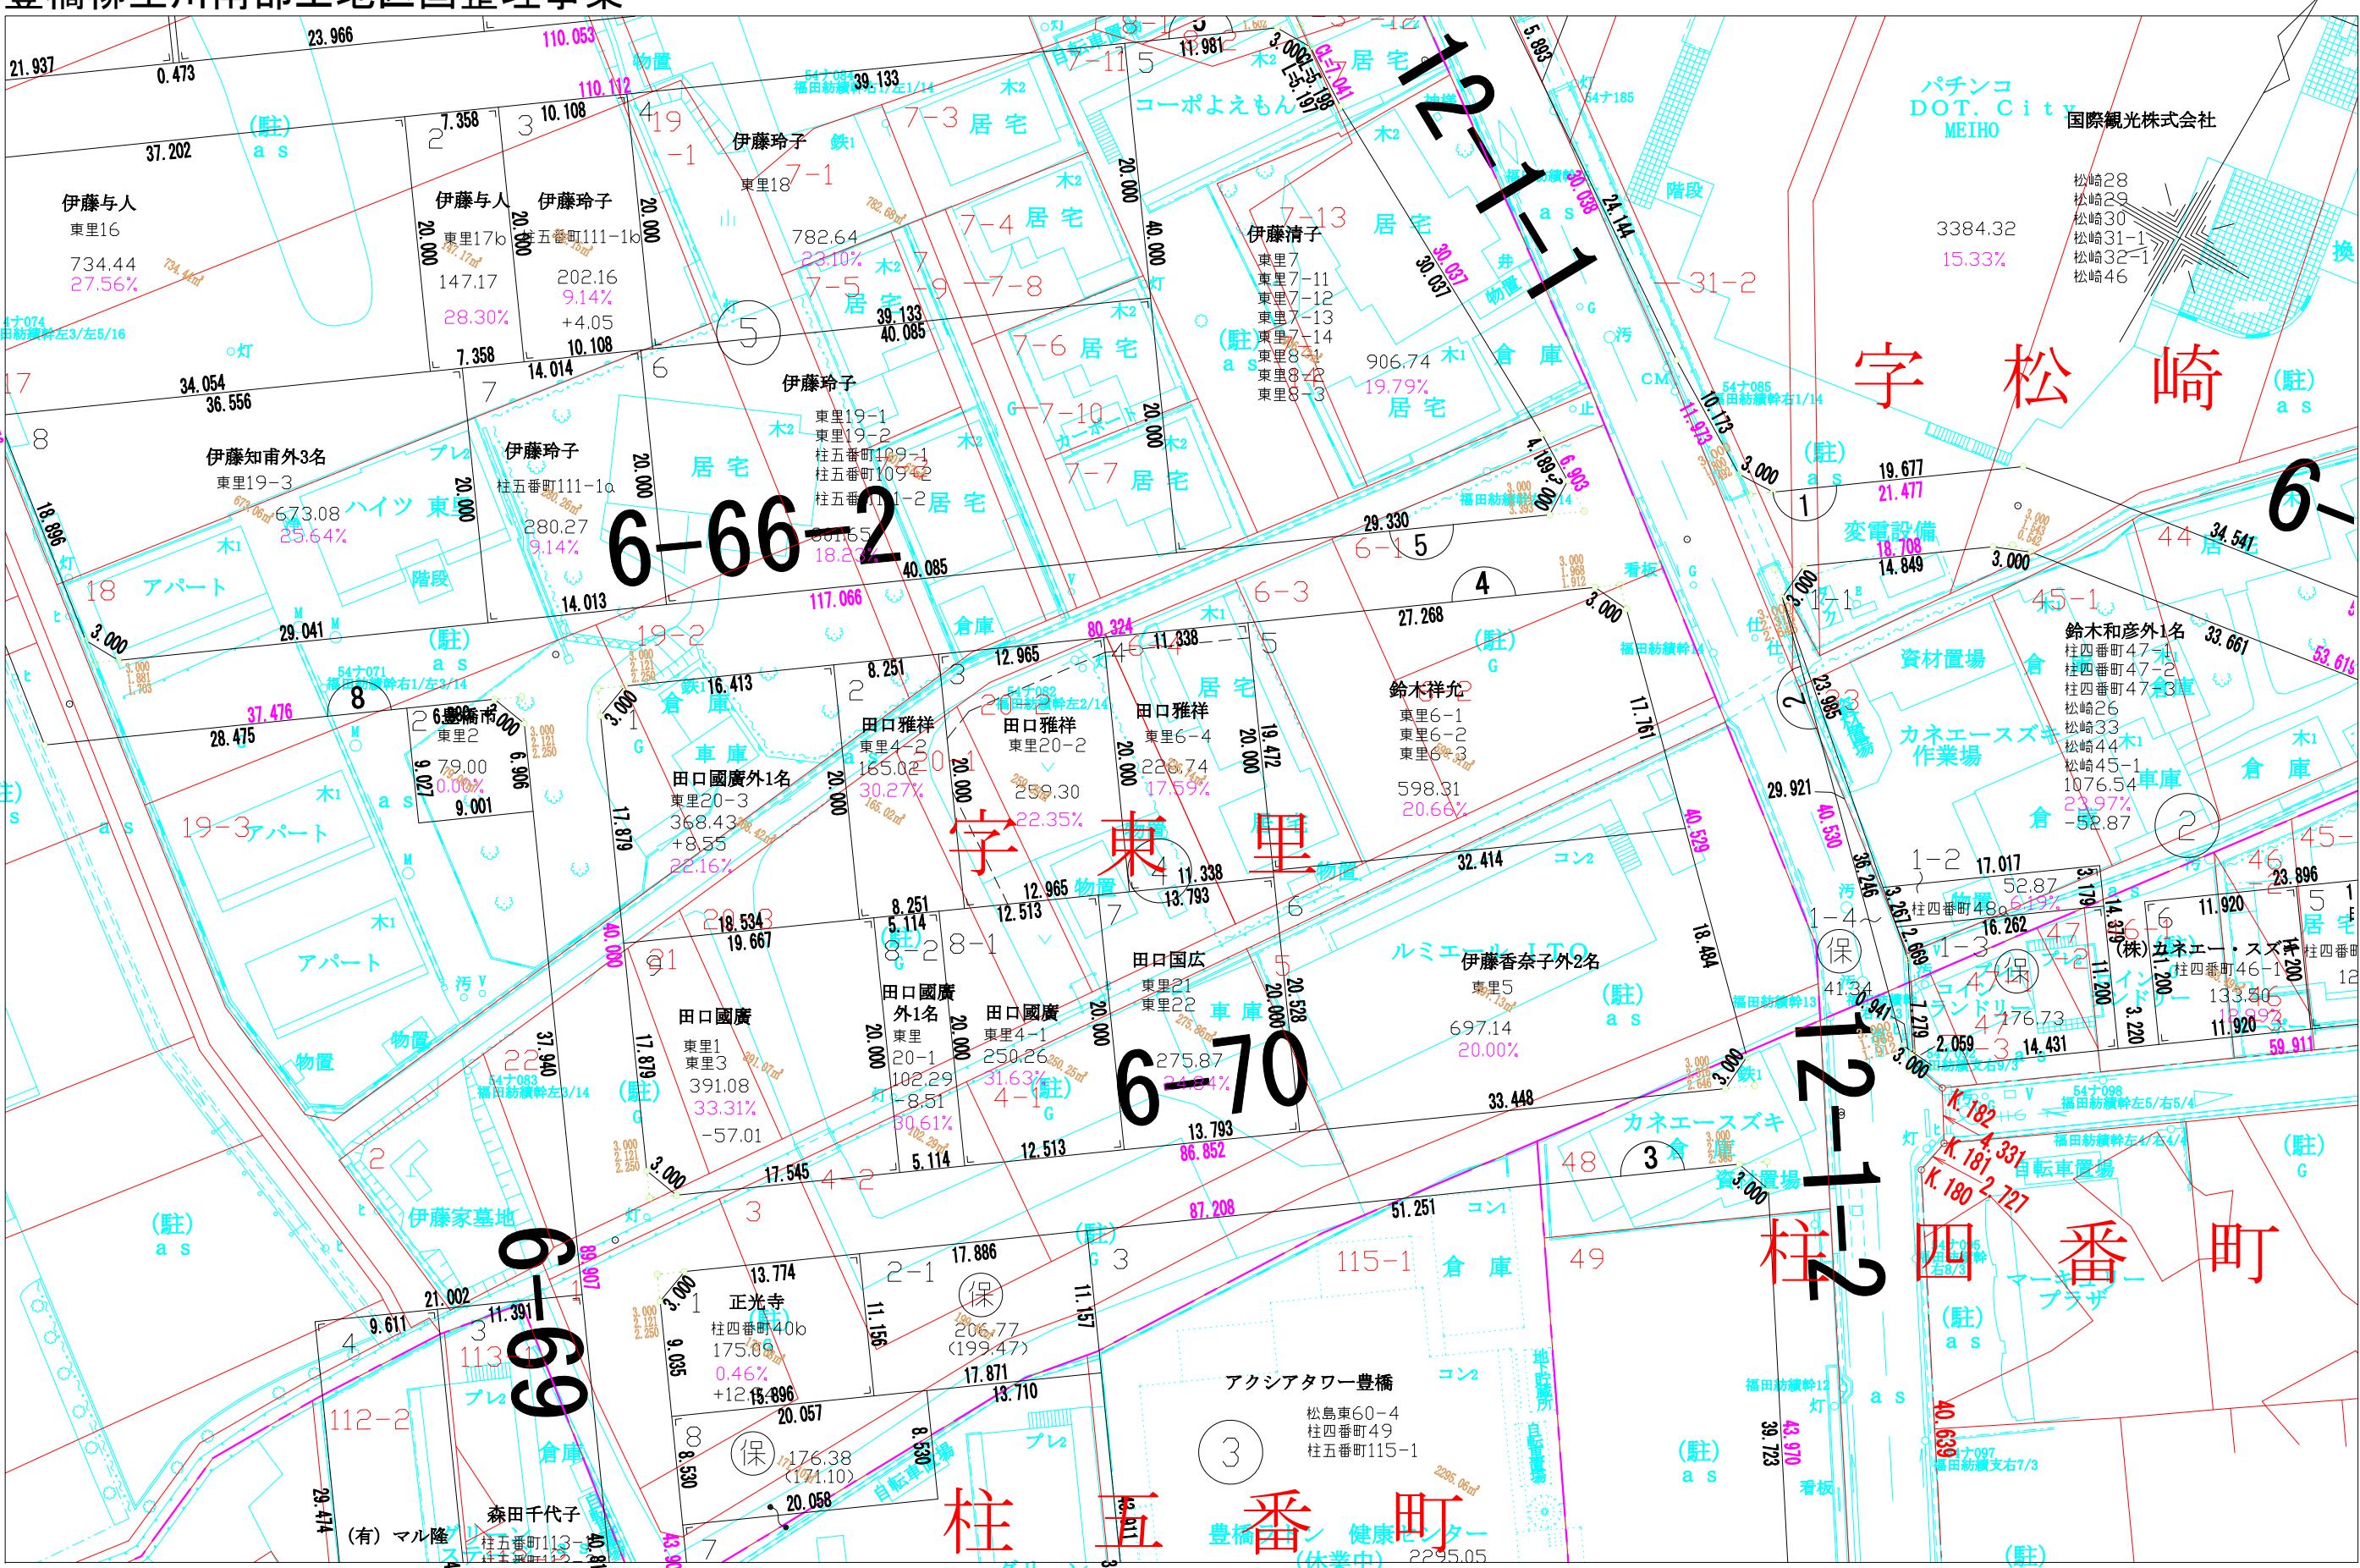


豊橋柳生川南部土地区画整理事業

重ね図（公図+現況+仮換地）

縮尺 500分の 1

5 街区

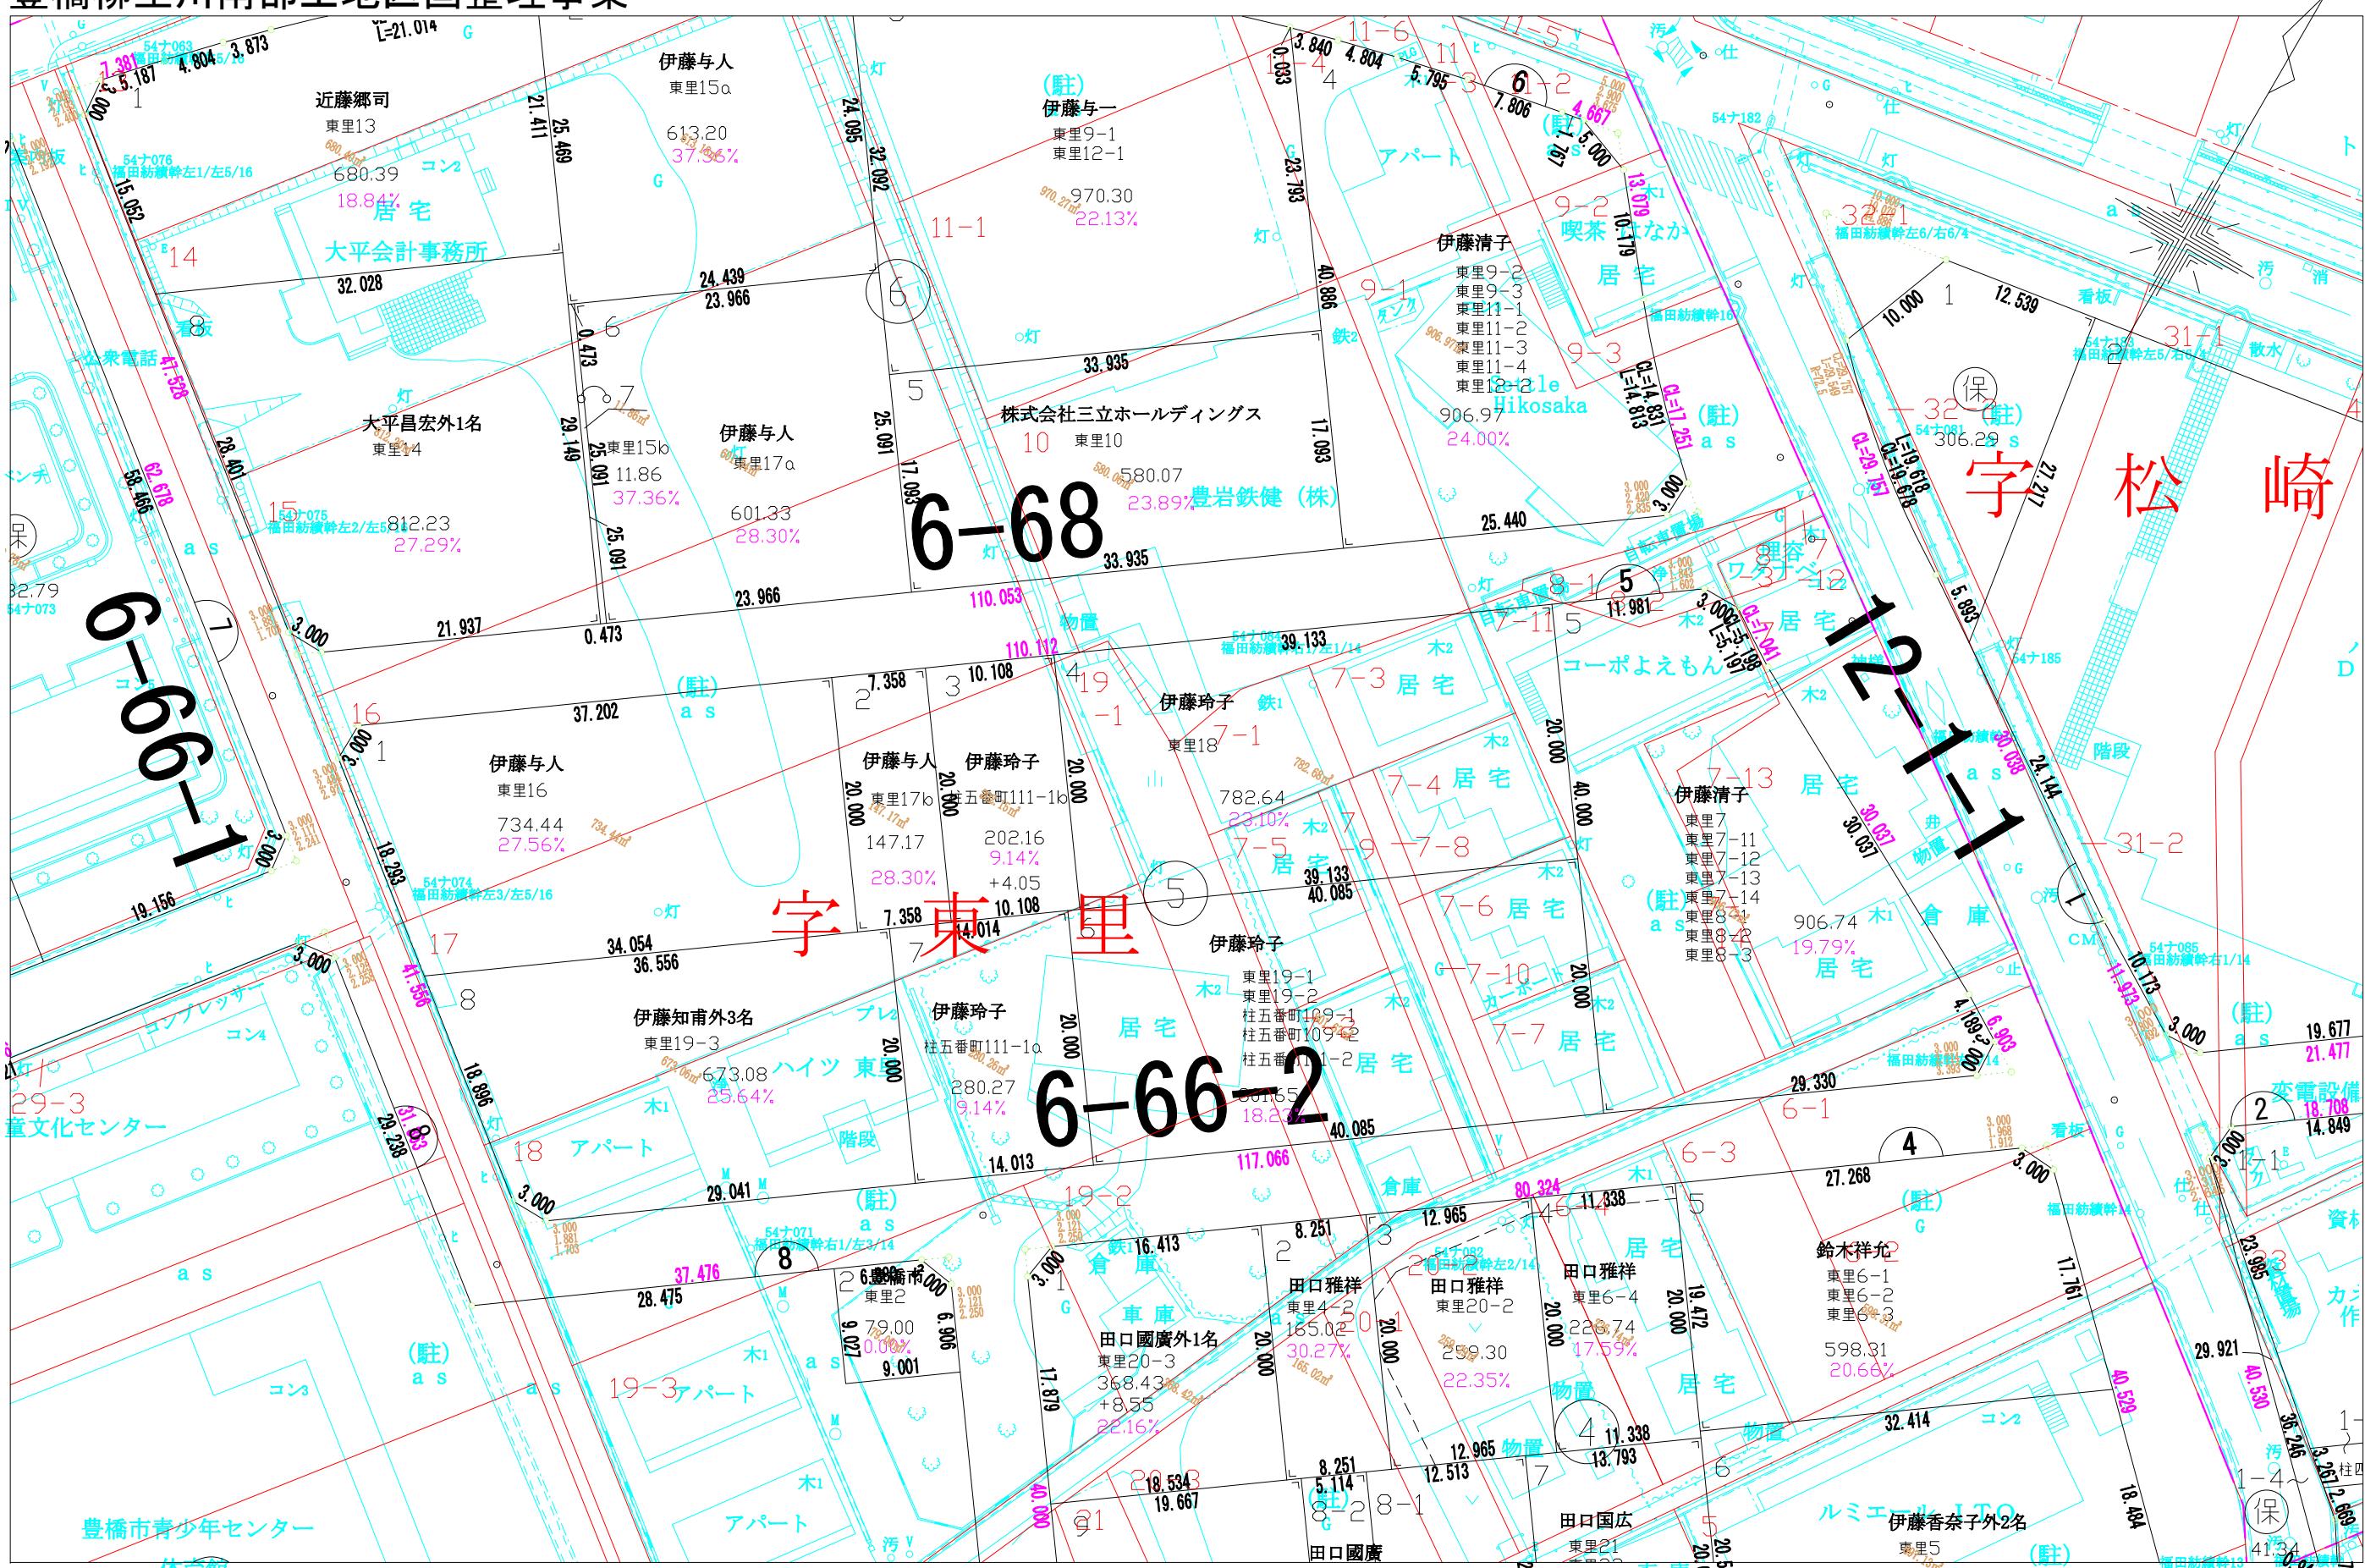


豊橋柳生川南部土地区画整理事業

重ね図（公図+現況+仮換地）

縮尺 500分の 1


6 街区

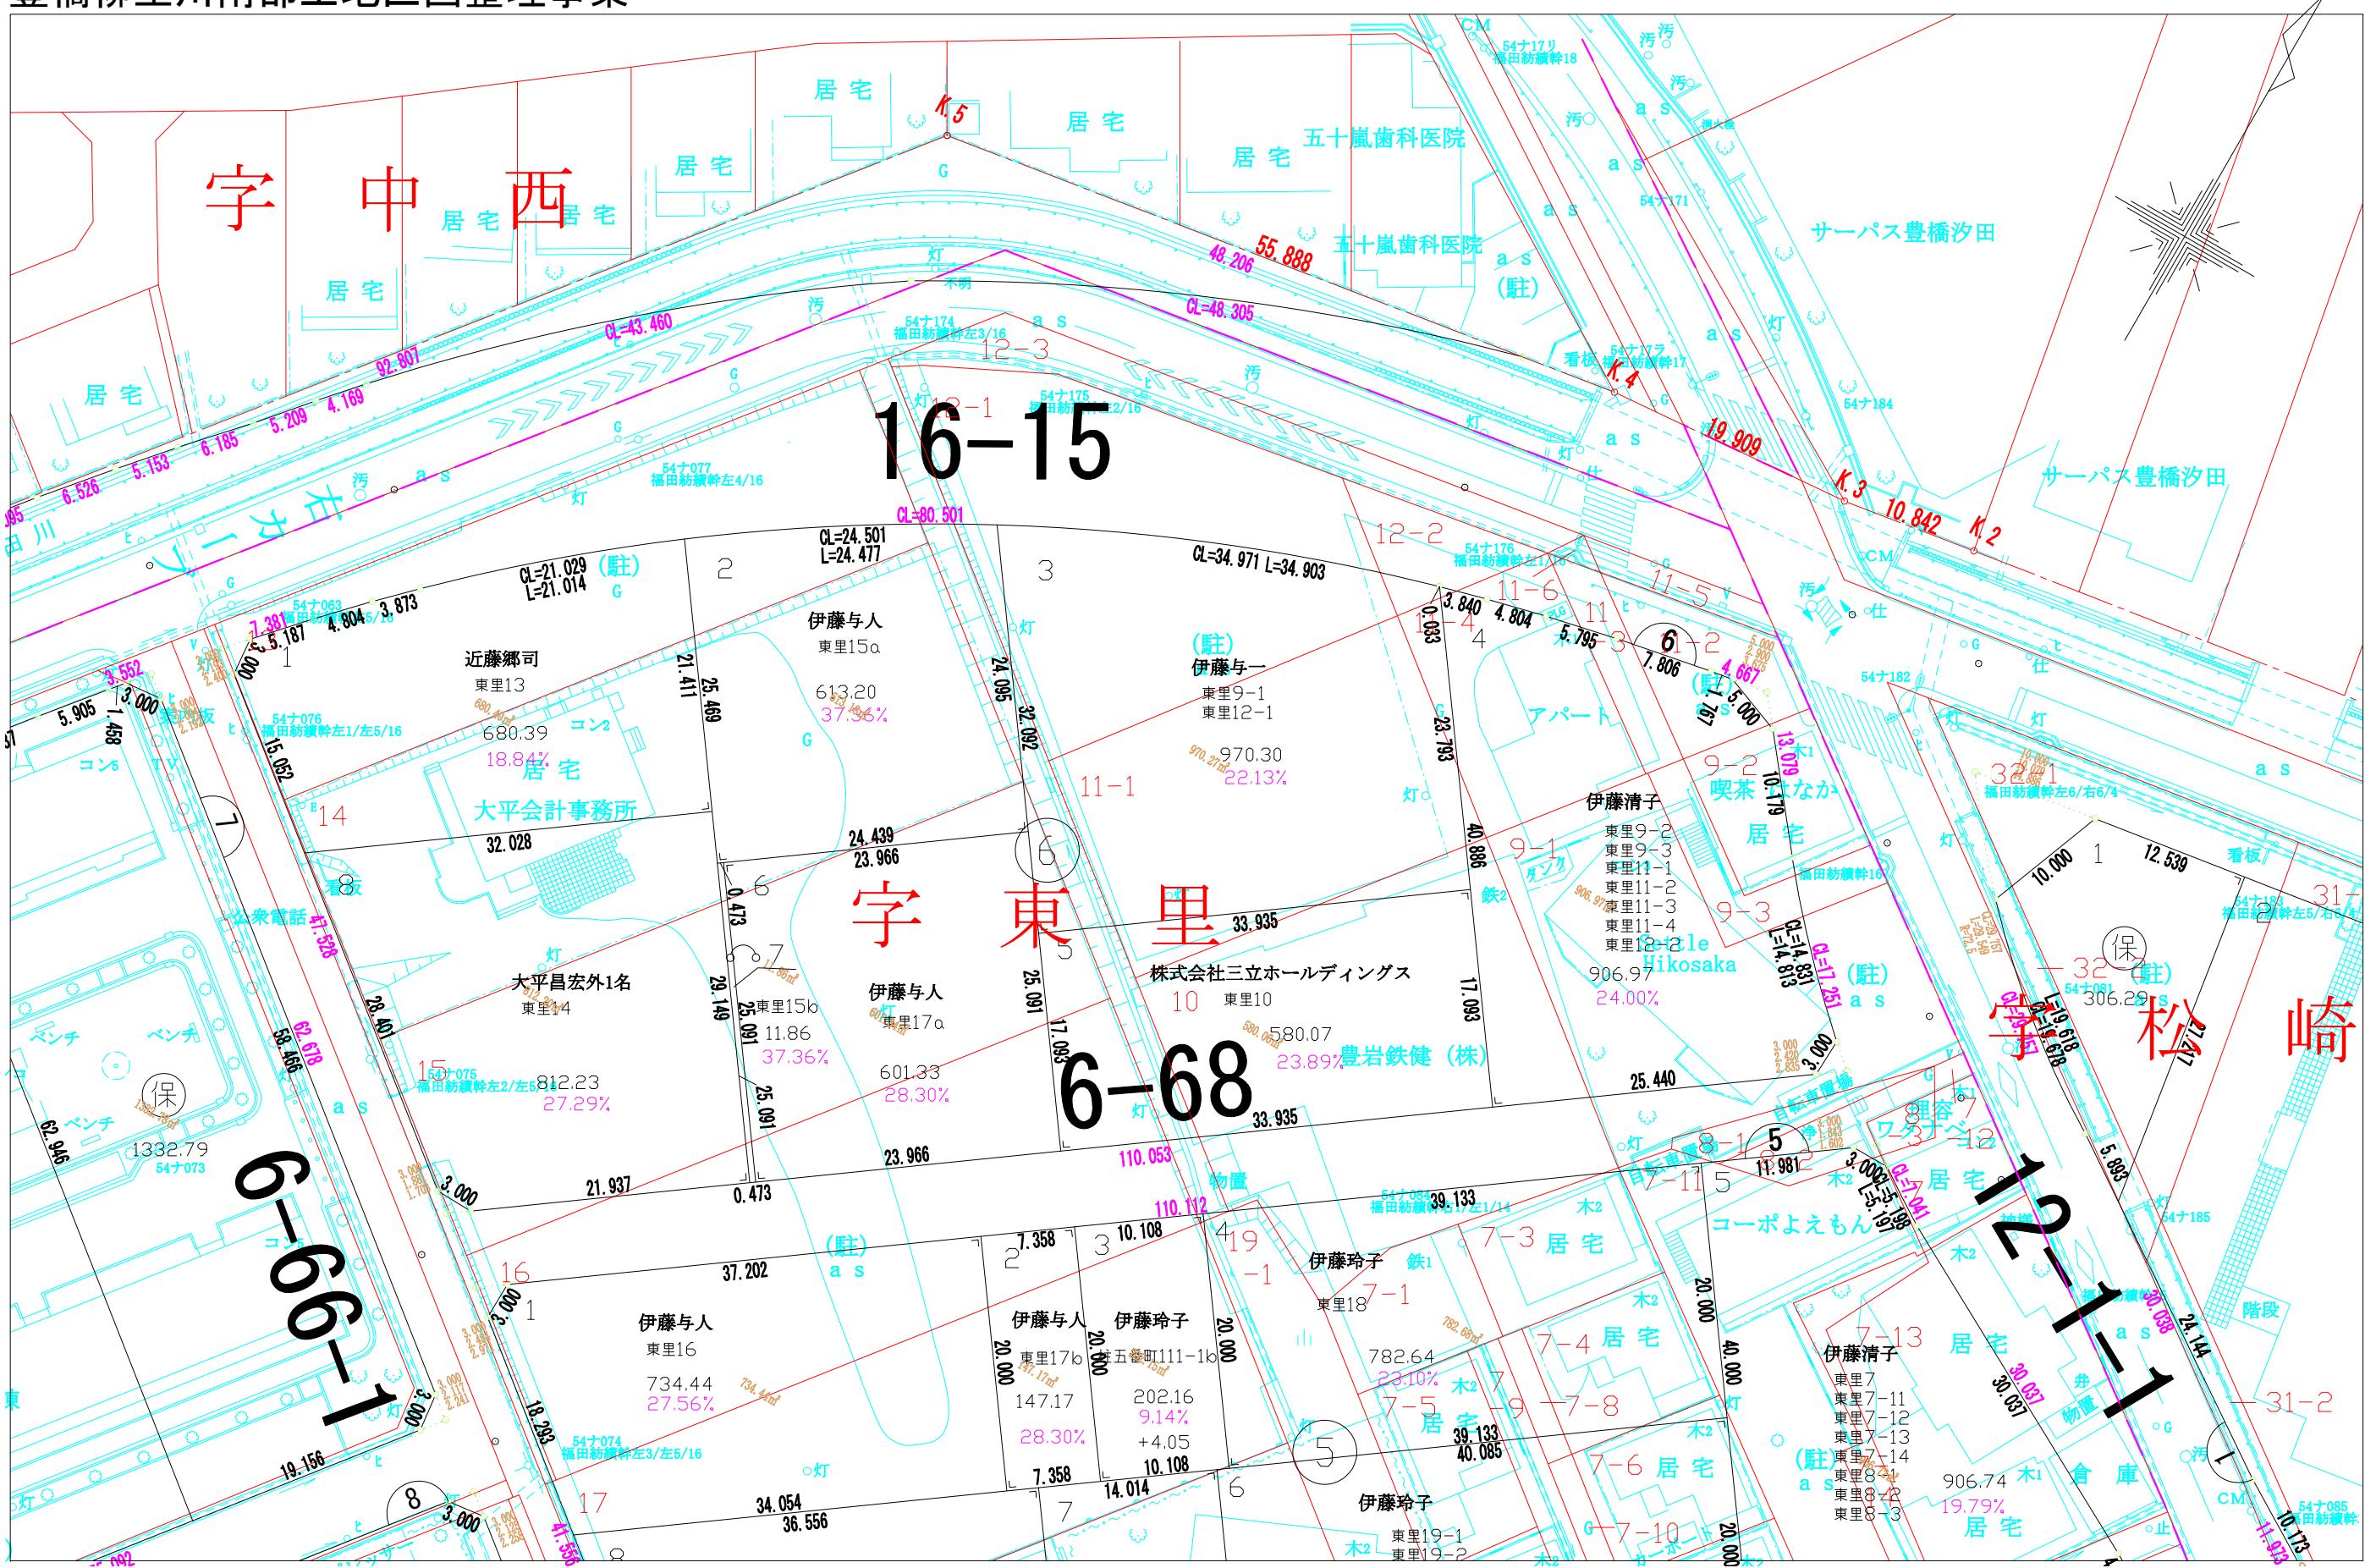

重ね図（公図+現況+仮換地）

7 街区

縮尺 500分の 1

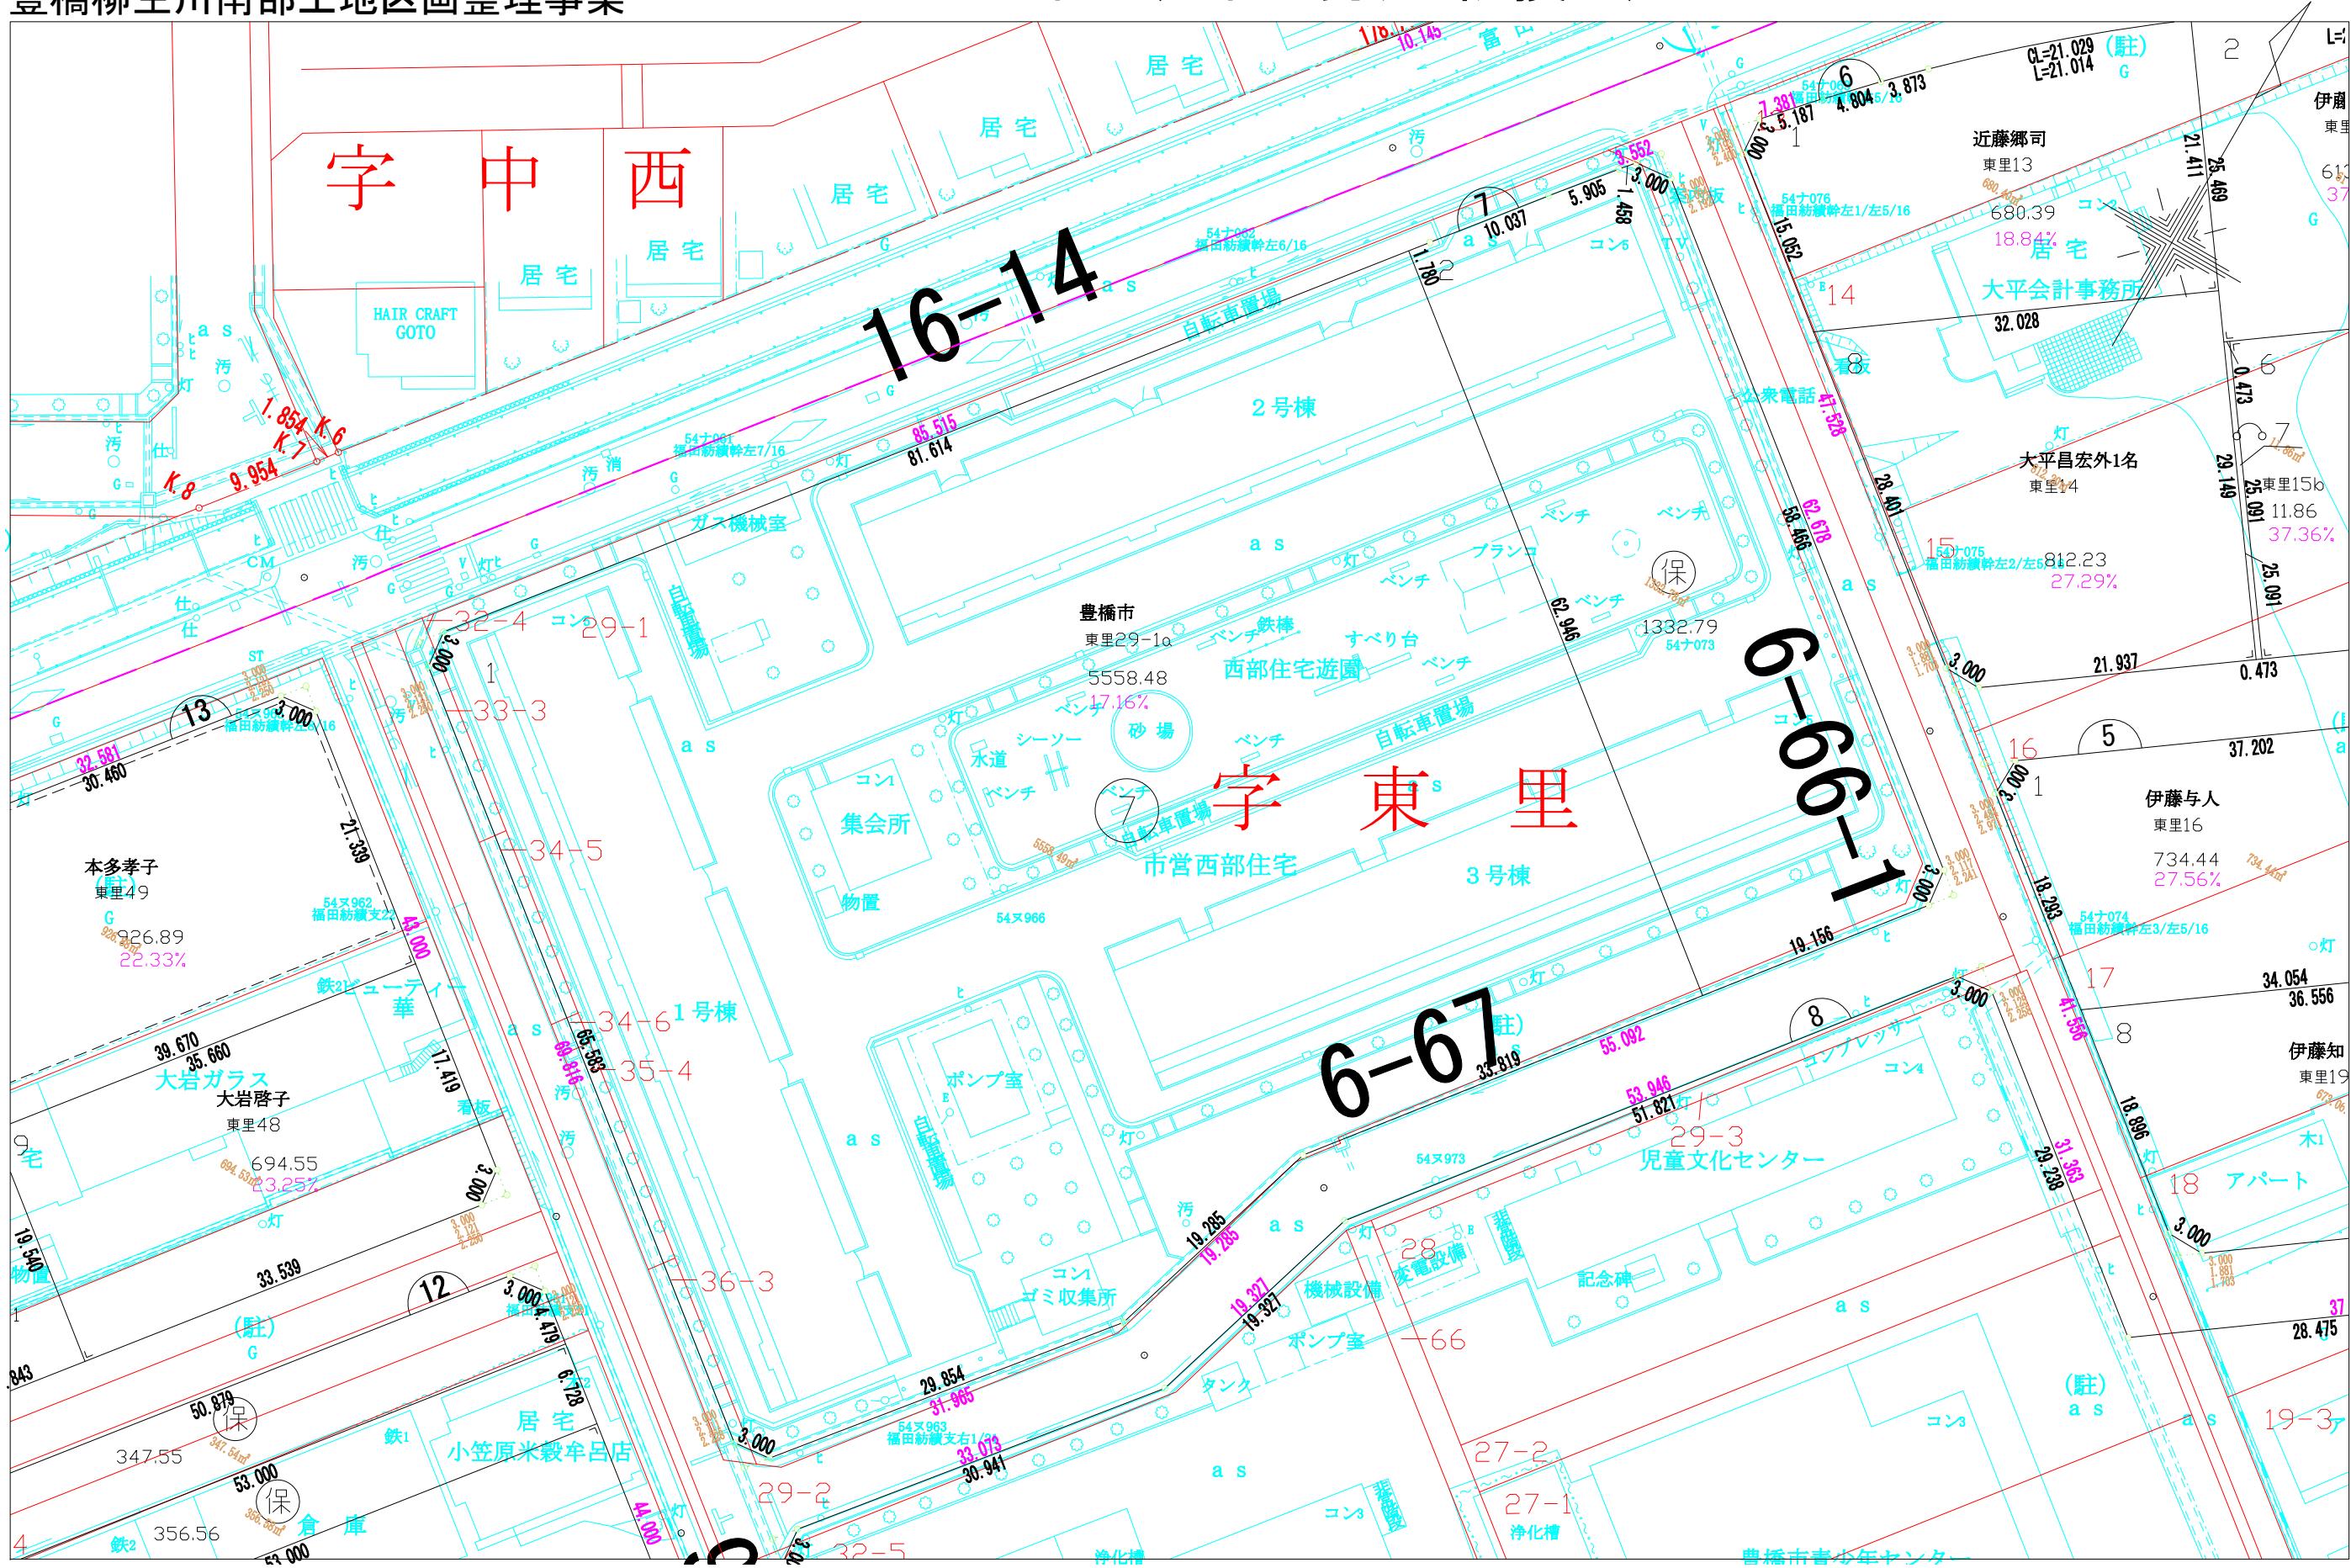

豊橋柳生川南部土地区画整理事業

重ね図（公図+現況+仮換地）

縮尺 500分の 1

8 街区

