
縮尺 500分の1

重 ね 図 (公図+現況+仮換地)

56 街区 小野広司 中村敏恵

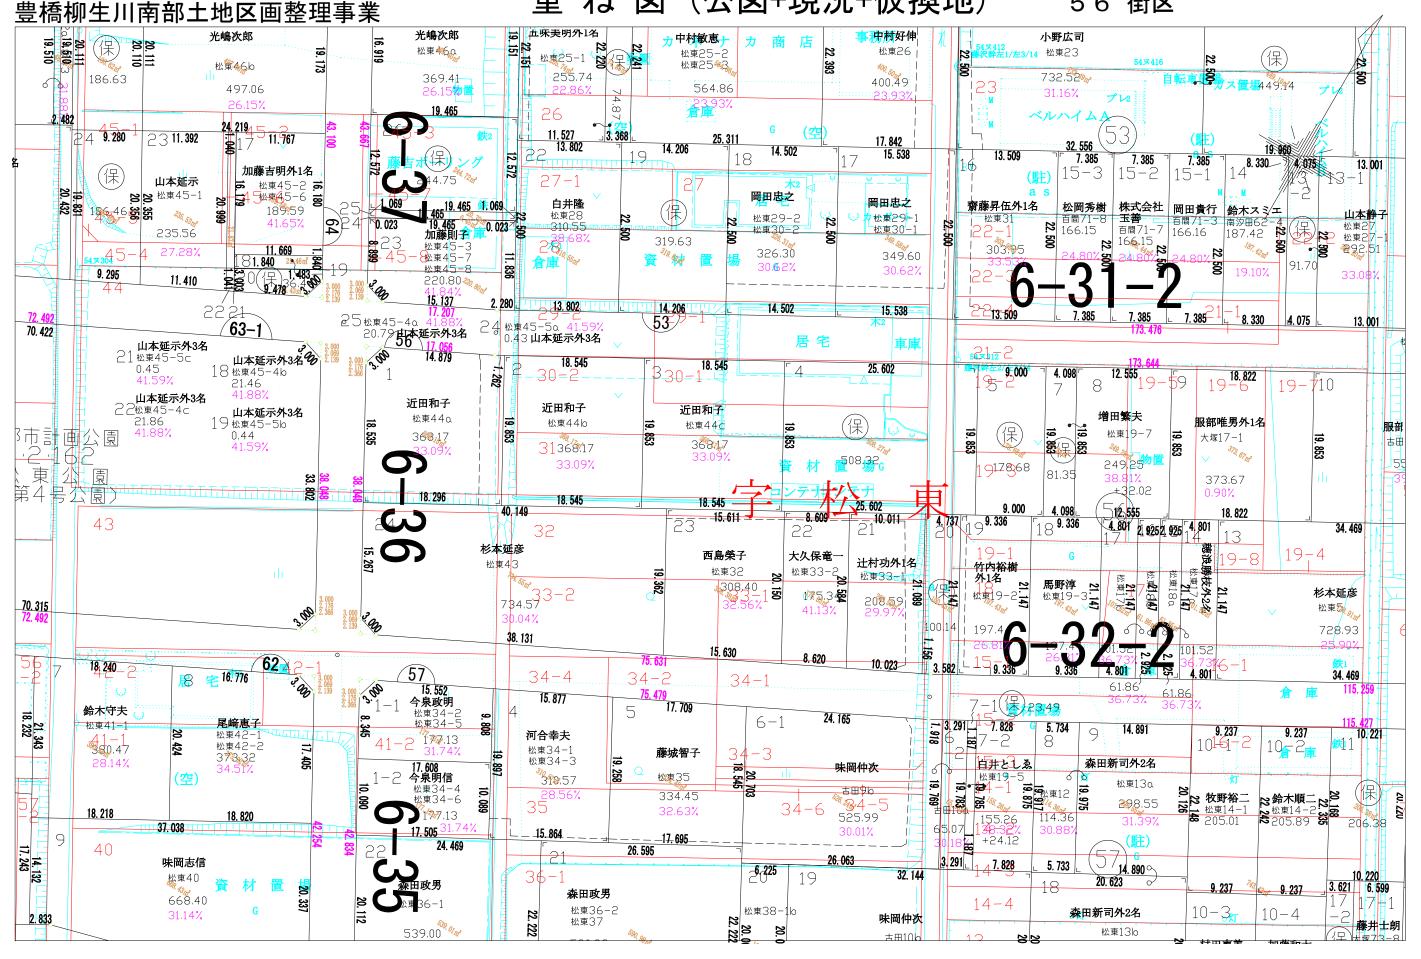

縮尺 500分の1 重 ね 図 (公図+現況+仮換地) 56 街区 豊橋柳生川南部土地区画整理事業 中村好伸 小野広司 中村敏恵 小柳津眞 服部智司 松東26 21/<u>左1/左3/14</u> 松東23 伊藤秀幸 松東25-2 保 21. 306 22. 500 夕1名 松東25%3 松東24 松東1 -255.74 732,52 400.49 616.05 616.05 置場44974 古田24-704.44 564.86 プル 31.16% 188.92 23.31% ベルハイム \mathbf{O} 17.842 32. 556 7. 385 13.802 14. 206 14. 502 19.960 **27. 380 2. 527** 12 11 15. 538 18 17 7. 385 33. 184 8. 330 4. 075 13. 001 16, 301 10 (駐) 13 - 13 27 - 1岡田忠之 岡田忠之 白井隆 齋藤昇伍外1名 松岡秀樹 株式会社 岡田貴行 保 鈴木スミエ 鈴木茂雄 山本静子 松東28 松東29-2 松東29-1 × 南汐田62-4 (早) 松東27 松東27 松東27 伊藤秀幸 310.55 松東3 百間71-7 | 166.16 松東30−1 166.15 23. 694 22. 500 187. 42m 319.63 166,15 松東2 8 . S • දි **292.5**1 303,95 366476 326,30 349.60 5 119.02 30.62% 784.81 30.62% 19.10% 31.17% 13. 802 14.206 14.502 15. 538 13. 509 7. 385 7. 385 8. 330 4.075 13.001 16, 301 31. 127 2.527 松島東6.4k 山本延示外3名 居宅 53/ **521**₁₂ 2 18, 545 18. 545 25, 602 **56** β_{30-1} 9,000 4.098 12. 555 30=2 27. 764 J-19-59 TO THE STATE OF TH 19-710 35. 333 11 近田和子 近田和子 増田繁夫 (保) 服部唯男外1名 松東44b 松東440 服部唯男外1名 (保) 服部唯男外1名 19.853 松東19-7 大塚17-1 ±⊞22 55 **E** E 36847 31368.17 松東4-1 8 සු 17. 734 松東4-2 ₹08.32_G 551.19 33.09% 249 25 <u>91.78</u>268 81.35 373.67 741.81 ±32.02 18, 545 27.48% 25. 602 9,000 555 <u>12.</u> 18. 822 21 10.011 ▶ 27. 764 **— 8. 609** – 4. 737 7 9. 336 37. 507 4.80 2 9252 925 4.801 34, 469 32 43. 024 19-4 西島榮子 大久保竜一 辻村功外1名 竹内裕樹 外1名 松東33-1 21.147 **等技外2名** 松東17 松東18 松東18 松東18 松東18 松東18 松東17 松東18 松東18 松東32 松東33-2 選 362 馬野淳 308,40 杉浦康夫 8 松東9-2-1 33-2 杉本延彦 19.023 1775,3餐 松東6 松東為 197 728.93 908,22 1.156 26.73% 15. 630 8. 620 O 400 34-4 34. 469 34-2 34-1 40.959 61.86 61,86 倉 残土 15. 877 資材置場 7-1(体)2349 17. 709 5 24. 165 6 - 1**57** 7. 828 5. 734 14.891 9 9. 237 <u>7. 631</u> 9. 237 **何合幸夫** 10. 221 800 33, 602 101-67-2 10=2 12-2 公東34-1 13 藤城智子 -3 公東34-3 森田新司外2名 白井としゑ 味岡仲次 20. 703 18. 545 大野栄二 鈴木将浩 松東35 319.57 19. 769 松東13a 19. 785 665 26₆₄ 19.975 19.875 古田りん 334.45
 5.2
 牧野裕二
 2
 鈴木順二
 2

 1
 松東14-1
 2
 松東14-2
 2

 2
 205.01
 205.89
 3
21.00 20.220 25.00 20.220 27.00 20.220 298.55 34-6 32.63% 味岡幸代 525,99 155.26 206.38 160.09 179.67 松東7 23, 422 15.864 _1**7. 695**_ +24.12 (駐) 907.70 30-1 26. 595 21 26.063 3. 291 <u>√ 7. 828</u> 5. 733 **_6_225** <u> 14. 890 ∽</u> 32, 144 10. 220 1 6. **5**99 19 7. 631 20. 623 8. 530 18 3. 621 9. 237 9, 237 森田政男 14 - 412-4 12 - 3松東36-2 松東38-1b 10 - 3森田新司外2名 10 - 4味岡仲次 20. 0 22. 222 松東37 藤井士朗 江藤和徳 新妻吾郎 8. 580 松東13b 豊橋柳生川南部土地区画整理組合 56 BLock 2-2